


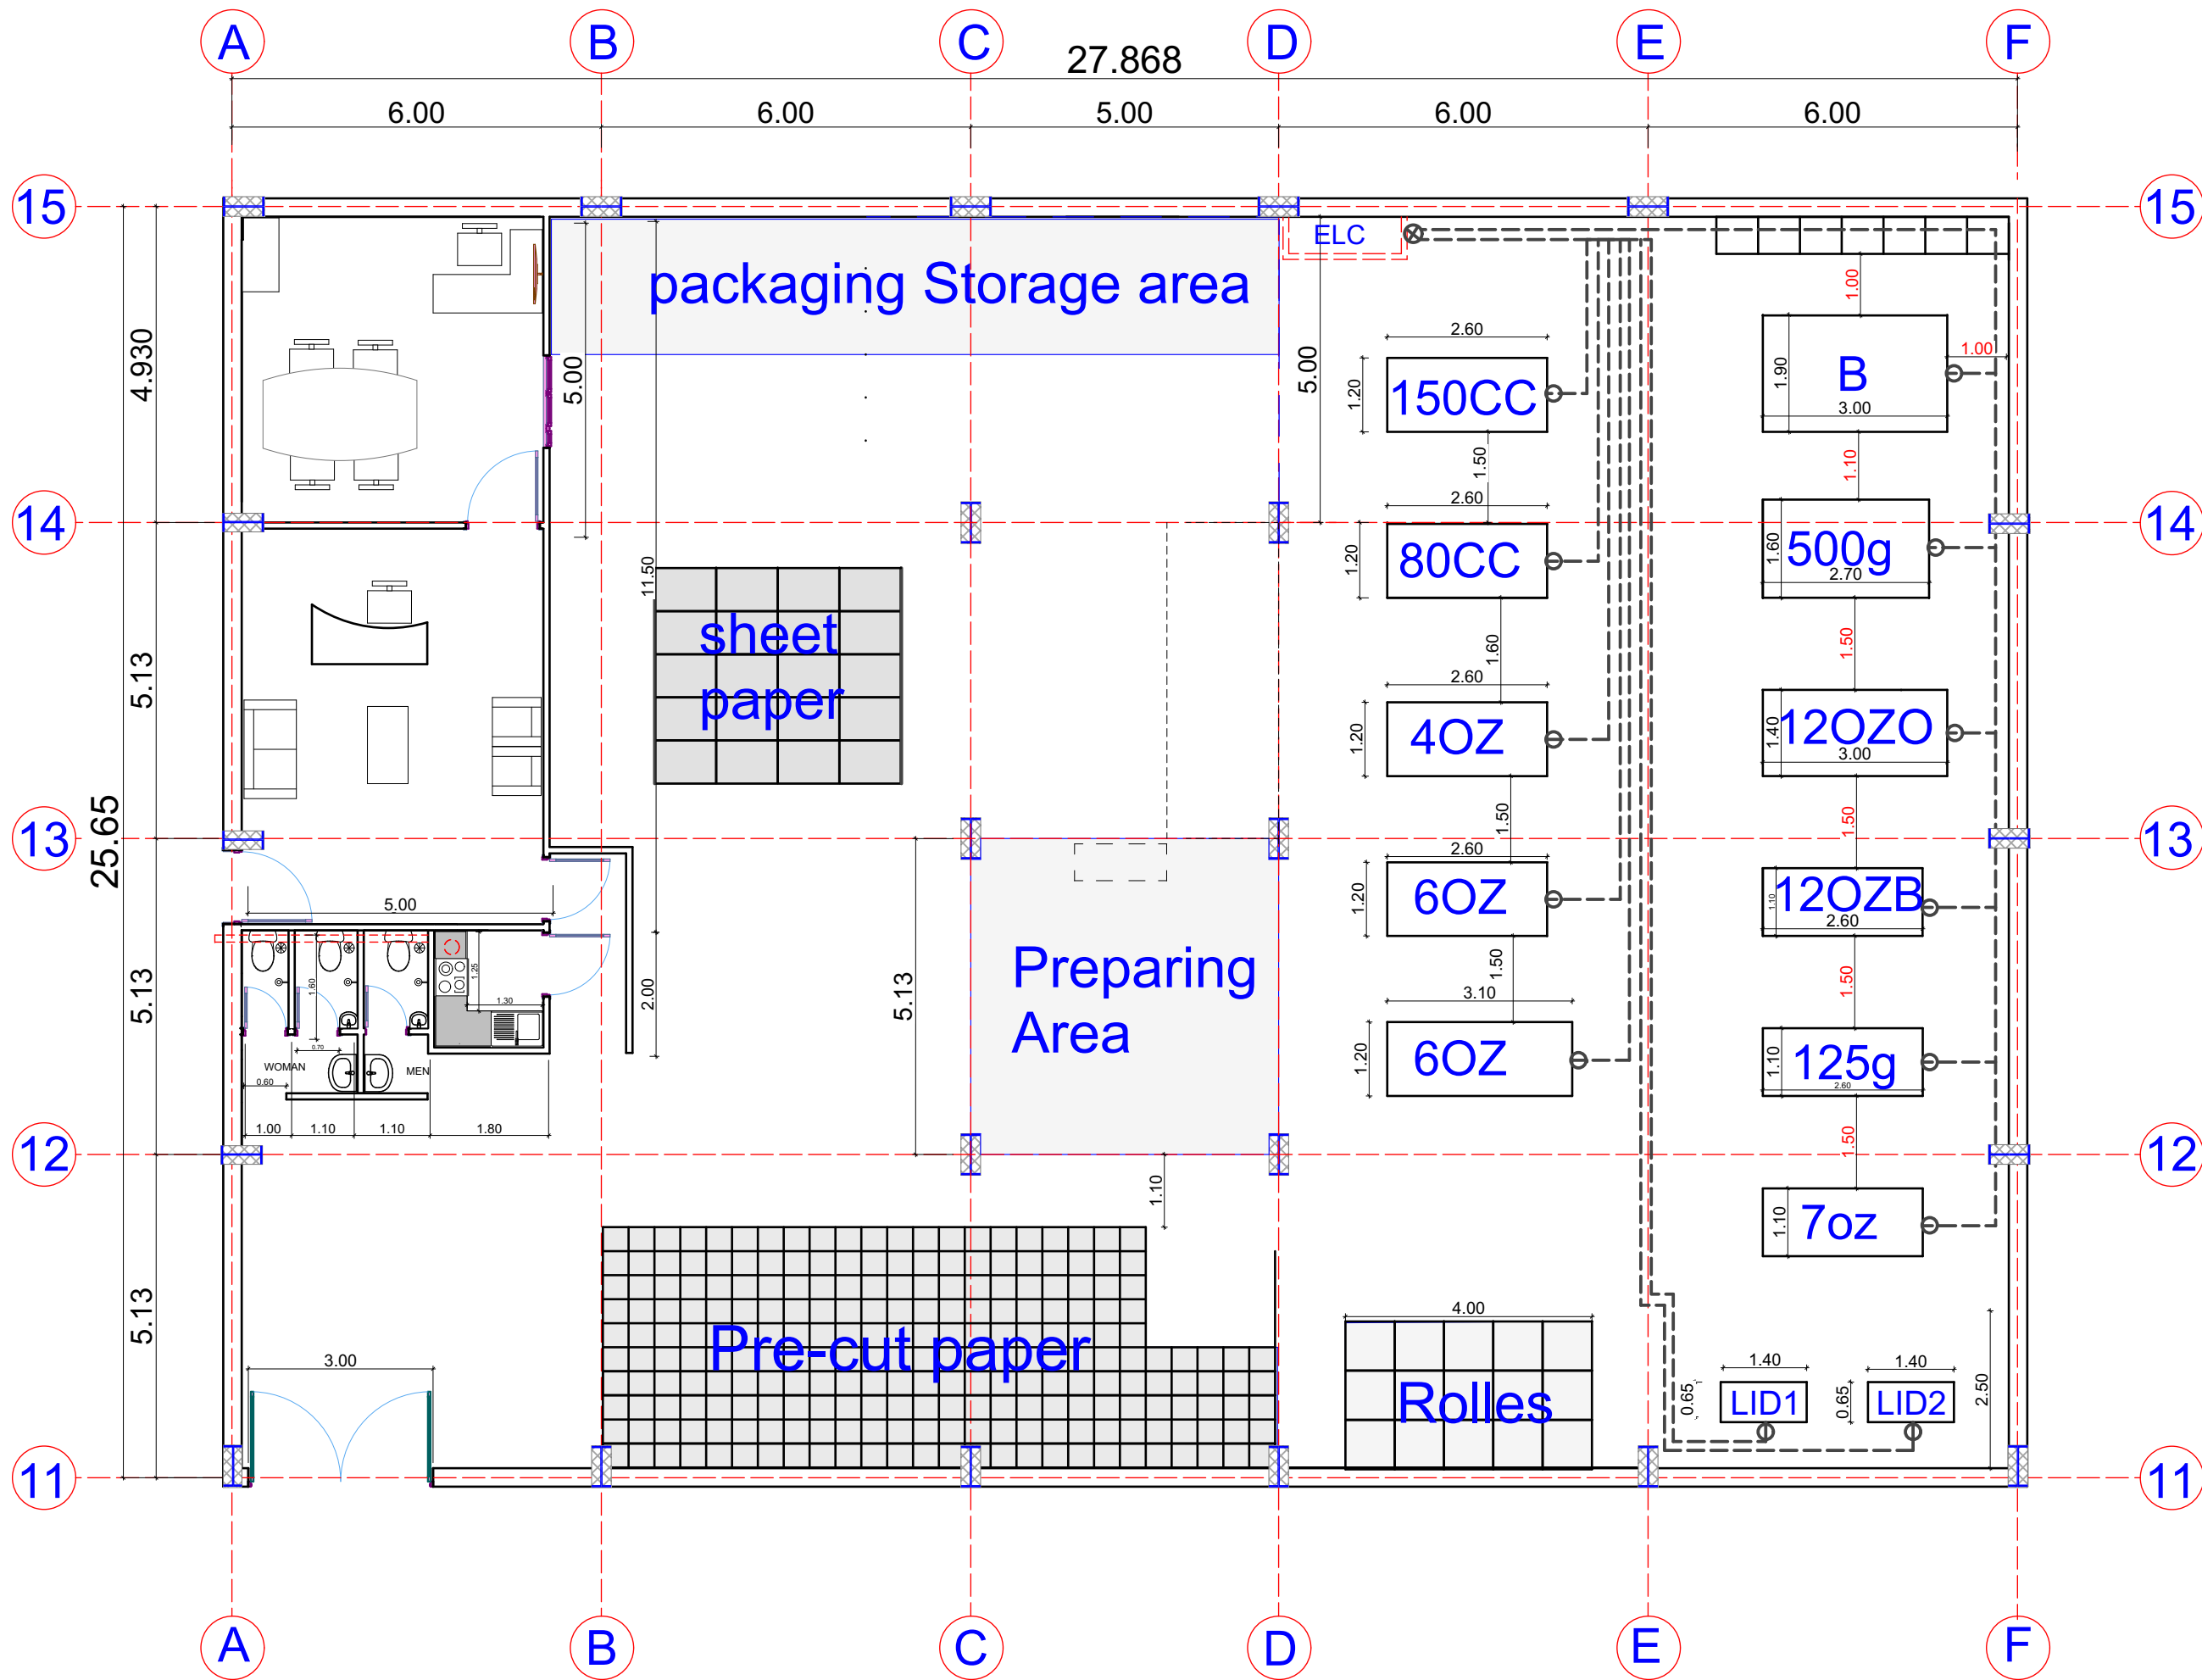

FIRST FLOOR PLAN



1. ALL DIMENSIONS SHOWN HEREIN AND ALL LEVELS ARE IN METERS UNLESS OTHERWISE NOTED.
2. ASSUME FINISH FLOOR LEVEL (FFL) AS EL. 0.00 OF GROUND FLOOR LEVEL. REFER TO SITE GRADING PLAN.
3. ALL DOORS & WINDOWS SHOWN ON PLANS SEE DRAWING DWGS FOR SCHEDULE OF DOORS, WINDOWS & PANELS.
4. VERIFY ALL SIZES/DIMENSIONS OF DOORS, WINDOWS & WINDOW OPENINGS ON THE JOBSITE AND SUBMIT SHOP DRAWINGS PRIOR TO FABRICATION AND INSTALLATION.
5. ALL SHOP DRAWINGS, SAMPLES, CATALOG CUTS ETC. TO BE APPROVED BY THE ARCHITECT BEFORE THE FINAL EXECUTION.
6. REFER TO MECH'L DWGS. FOR EXACT LOCATION AND SIZES OF ALL MECH'L ELEMENTS SHOWN ON FLOOR PLANS CEILING PLANS AND ROOF PLANS.
7. REFER TO ELECT'L DWGS. FOR ALL TYPES OF ELECT'L ELEMENTS & LIGHTING FIXTURES.
8. FOR EXTERNAL WORKS I.E. BOUNDARY WALL, FENCE AND OTHER RELATED ITEMS, REFER TO CIVIL DRAWINGS.
9. ANY DISCREPANCY ON SITE & SHOP DRAWINGS REFER TO CONSULTING ARCHITECT.



SYRIAN HOUSE

Ozone Back

PLOT NO.	BLOCK NO.	TOWN
		KHARTOUM BAHREY

PROJECT TITLE

SYRIAN HOUSE FACTORY

DRAWING TITLE

FIRST FLOOR
ARCHITECTURAL DRAWINGS
LAYOUT PLAN

SCALE:1 :100